
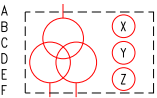
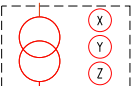


	LÁMPARA DE PRESENCIA DE TENSIÓN
	TRANSFORMADOR POTENCIA TRES DEVANADOS: A: TAG DEL EQUIPO B: POTENCIA NOMINAL (kVA) C: RELACIÓN DE TRANSFORMACIÓN. D: TIPO DE ENFRIAMIENTO. ONAN: OIL NATURAL AIR NATURAL E: GRUPO DE CONEXIÓN. F: IMPEDANCIA DE CORTOCIRCUITO (%) X, Y, Z: PROTECCIÓN DEL TRANSF.
	INTERRUPTOR MEDIA TENSIÓN TIPO FIJO A: CAPACIDAD DE CORRIENTE (A). B: TENSIÓN NOMINAL (kV). C: CAP. RUPTURA CORTOCIRCUITO (kA). D: TENSIÓN ENSAYO IMPULSO RAYO (kV).
	MEDIDOR DE ENERGIA MULTIFUNCIÓN MODELO 10N 7400
	SECCIONADOR, OPERACIÓN SIN CARGA. A: CAPACIDAD DE CORRIENTE (A). B: TENSION NOMINAL (kV). C: NIVEL DE AISLAMIENTO (kV).
	TRANSF. CORRIENTE DE FASE: A: RELACIÓN TRANSF. B: BURDEN (VA). C: CLASE PRECISIÓN (MEDICIÓN). D: BURDEN (VA). E: PRECISIÓN (PROTECCIÓN) F: TENSIÓN ASIGNADA (kV). H: TENSIÓN ENSAYO AL RAYO (kV)
	TRANSF. CORRIENTE SEC. CERO. CANTIDAD Y RELACIÓN TRANSF. A: RELACIÓN DE TRANSFORMACIÓN. B: CLASE. C: BURDEN, D: PRECISIÓN.
	PARARRAYOS TIPO ÓXIDO DE ZINC Ur: TENSIÓN ASIGNADA (kV). Uc: TENSIÓN SEV. CONTINUO (kV). C: CLASE D: CORR. NOM. DESCARGA (A).
	TRANSF. DISTRIBUCIÓN EN ACEITE. A: TAG DEL EQUIPO B: POTENCIA NOMINAL (kVA) C: RELACIÓN DE TRANSFORMACIÓN. D: TIPO DE ENFRIAMIENTO ONAN E: GRUPO DE CONEXIÓN. Dyn5 F: IMPEDANCIA CORTOCIRCUITO (%) X, Y, Z: PROT. TRANSFORMADOR.

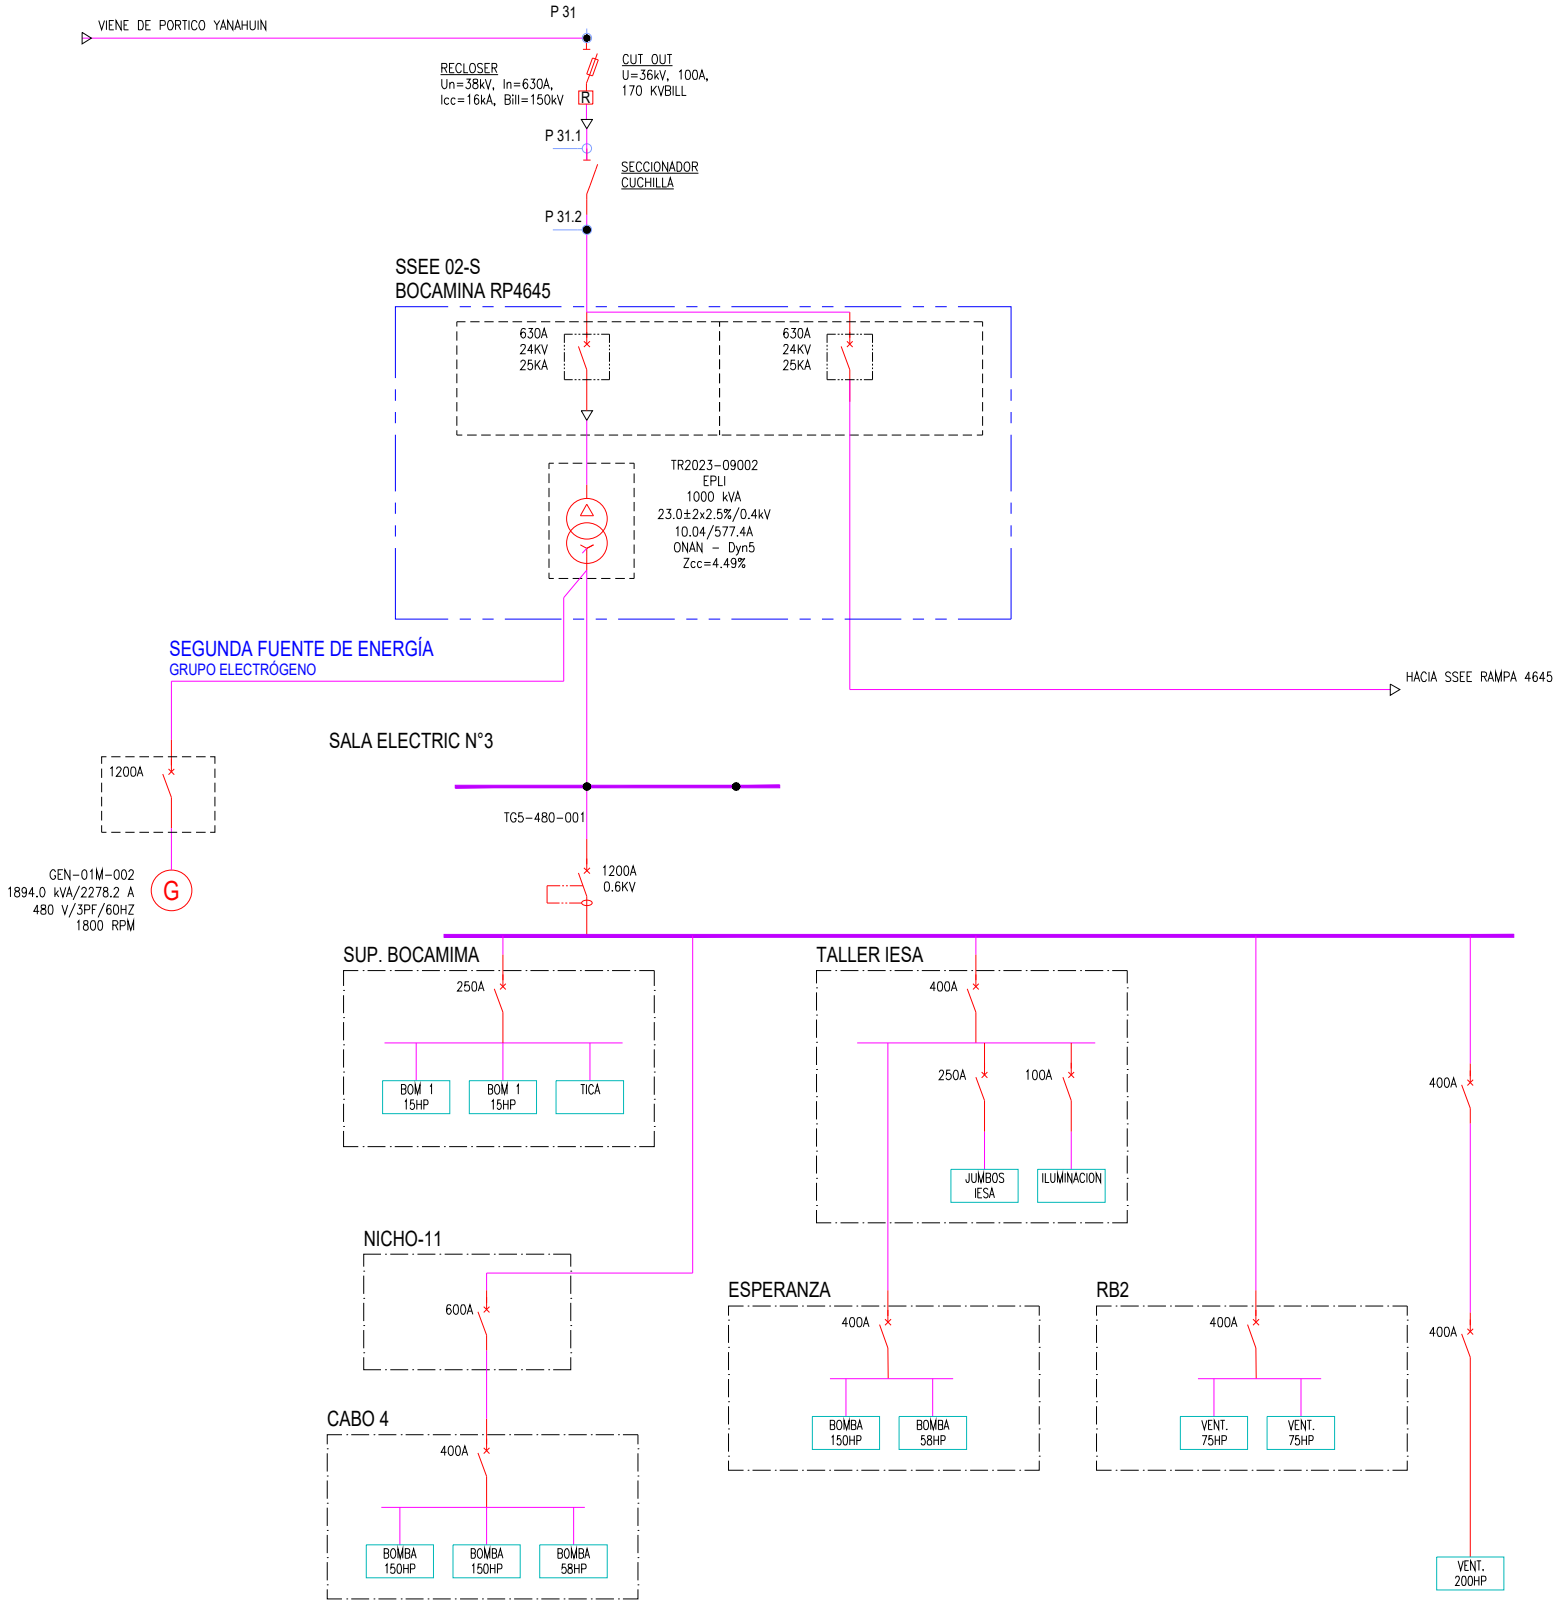

Este plano y su contenido son confidenciales, para información privada de VOLCAN. Sólo para utilizarse en el proyecto para el que fue preparado, y no debe ser utilizado en su totalidad o en parte para otros fines o en beneficio de otros sin la adaptación previa y verificación por escrito de "EMPRESA".																		DIBUJADO	W. INGAROCA		Proyecto	Copyright												
																														MINA ROMINA	Opcional:			
													1	SM	15-06-26	Actualización												REVISADO	R. HUAMANI	Título	SSEE 02-S SUBESTACION BOCAMINA RP4645			
													0	SM	20-04-26	Actualización													ACTUALIZ.	W. INGAROCA	DIAGAMA UNIFILAR UNIDAD ROMINA	Plano N°		
													C	SM	20-04-26	Emisión para revisión																Escala:	INDICADA	Tamaño:
			B	SM	04-04-26	Revisión por Jefectura												REVISADO POR JEFACTURA	R. HUAMANI	SISTEMA ELÉCTRICO 22.9 KV	Plano de cliente N°		N° de Plano	REV										
			A	SM	04-04-26																			1/1	1									
Número de Plano	Planos de referencia	N°	Por	Fecha	Detalles de revisión			REV POR	DIB POR	APROB POR	PROYECTO APROBADO POR	MANTENIMIENTO ELÉCTRICO																						